

1. Baustufe


Bft Mü-Steinhausen

RSTW ESTW-Z Kz 46

Strecke 5603 km 2,700

Höhe: 527,8 m NN

- = DB Netz Bestand
- = Rückbau
-  = Werksgebiete DB Regio
-  = APS-Gleise
-  = Neubau
-  = Planung DB Regio (2019/20)

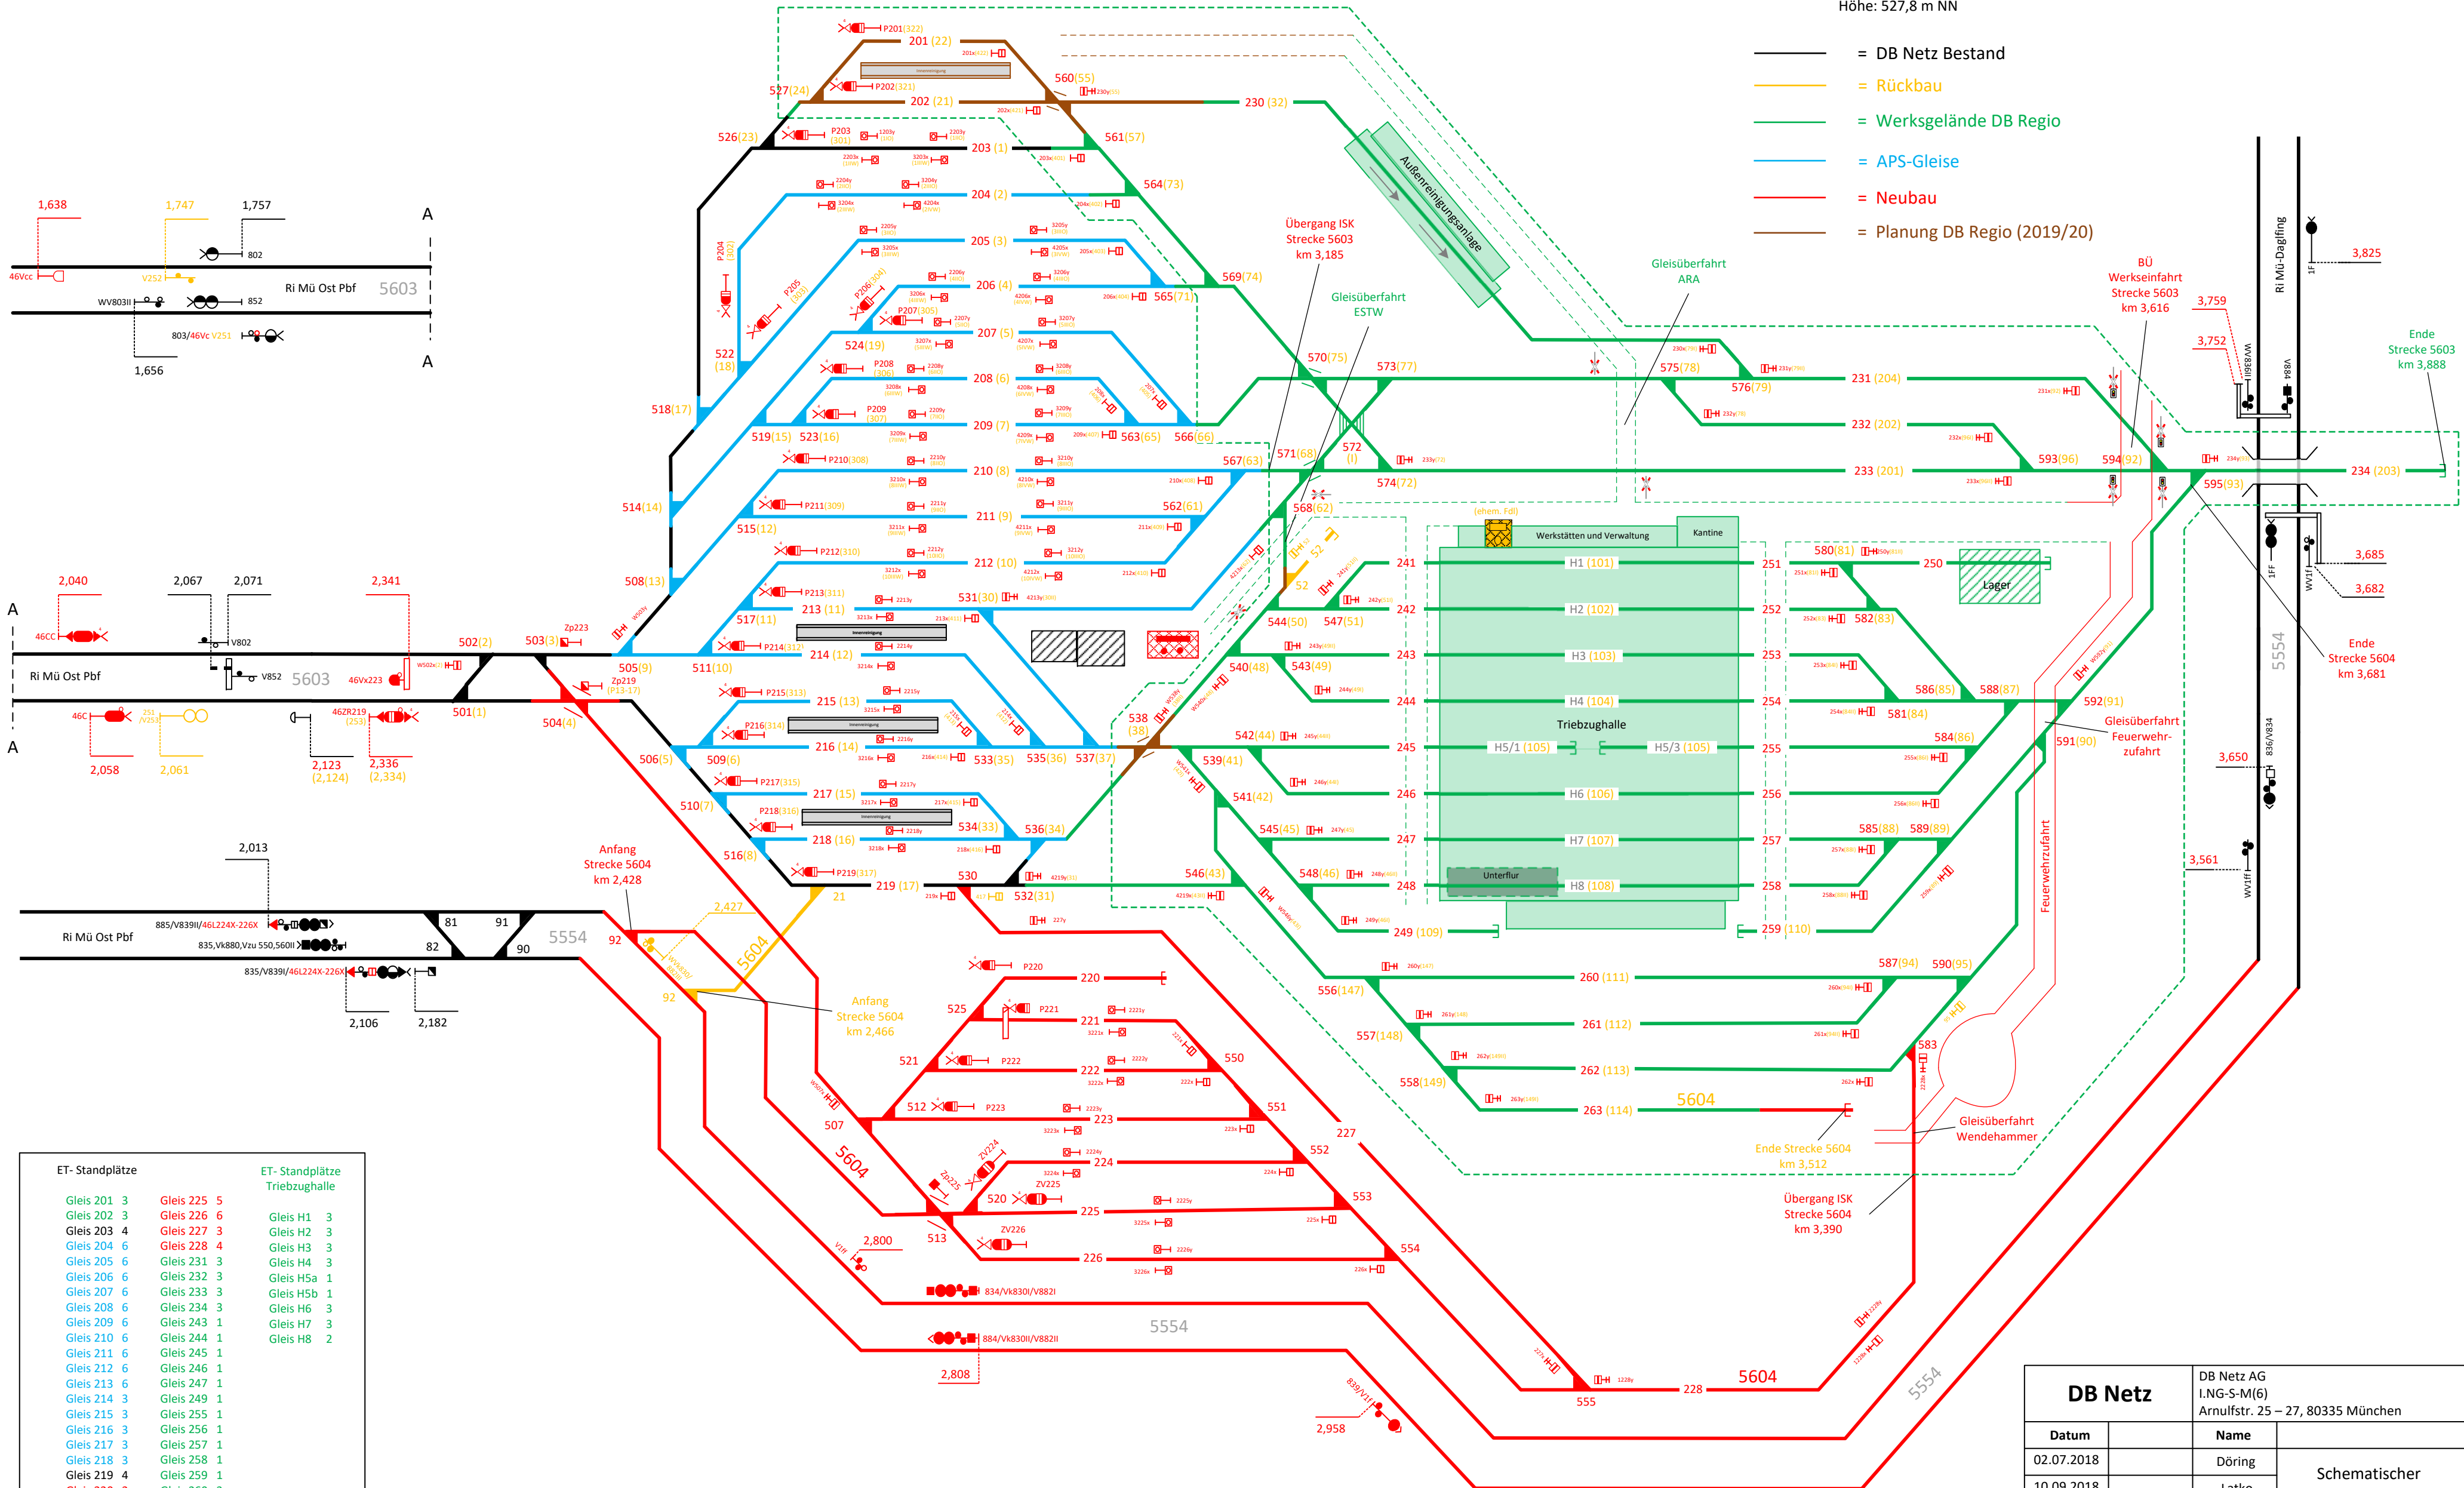

DB Netz		DB Netz AG I.NG-S-M(6) Arnulfstr. 25 – 27, 80335 München	
Datum		Name	Schematischer Lageplan Bft Mü-Steinhausen Erweiterung BS 1
02.07.2018		Döring	
10.09.2018		Latko	
29.09.2018		Döring	
29.01.2019		Döring	
20.02.2019		Döring	